Tabla de Iluminacion y Ventilacion de Locales

N°	Locales		Iluminacion			Ventilacion			Aberturas
	Nombre	Área	Coef. Ilum.	Ilum. Nec.	Ilum. Proy.	Coef. Vent.	Vent. Nec.	Vent. Proy.	
01	Dormitorio	20.27 m²	0.10	2.03	3.52	0.33	0.67	1.76	
02	Baño	1.60 m²	0.00	0.00	0.00	0.00	0.00	0.00	Art. 4.6.5.1.
03	Depo.	2.60 m²	0.00	0.00	0.00	0.00	0.00	0.00	Art. 4.6.5.1.
04	Lav.	4.33 m²	0.00	0.00	0.00	0.00	0.00	0.00	Art. 4.6.5.1.
05	Cocina - Living - Comedor	61.17 m²	0.10	6.12	16.26	0.33	2.02	8.13	
06	Baño	3.50 m²	0.10	0.35	0.96	0.33	0.12	0.48	
07	Baño	3.50 m²	0.10	0.35	0.96	0.33	0.12	0.48	
08	Dormitorio	11.16 m²	0.10	1.12	3.52	0.33	0.37	1.76	
09	Dormitorio	11.16 m²	0.10	1.12	3.52	0.33	0.37	1.76	

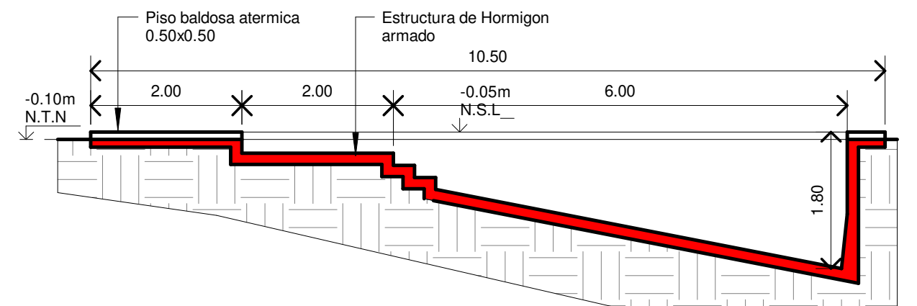
Piso baldosa atermica 0.50x0.50
Estructura de Hormigon armado
-0.10m N.T.N
-0.05m N.S.L
2.00
2.00
6.00
1.80

CORTE PILETA

1 : 100

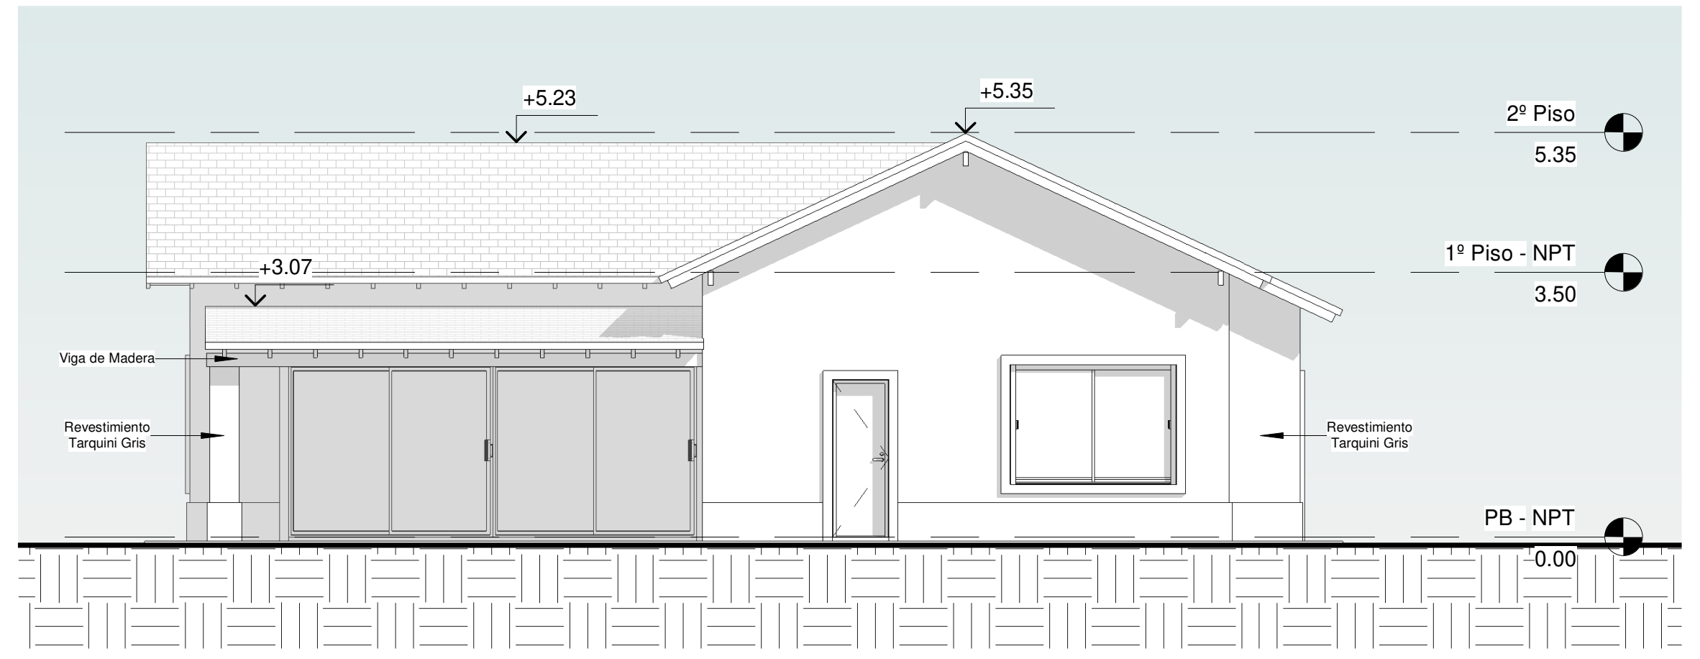

4 Vista Contrafrente

1 : 100

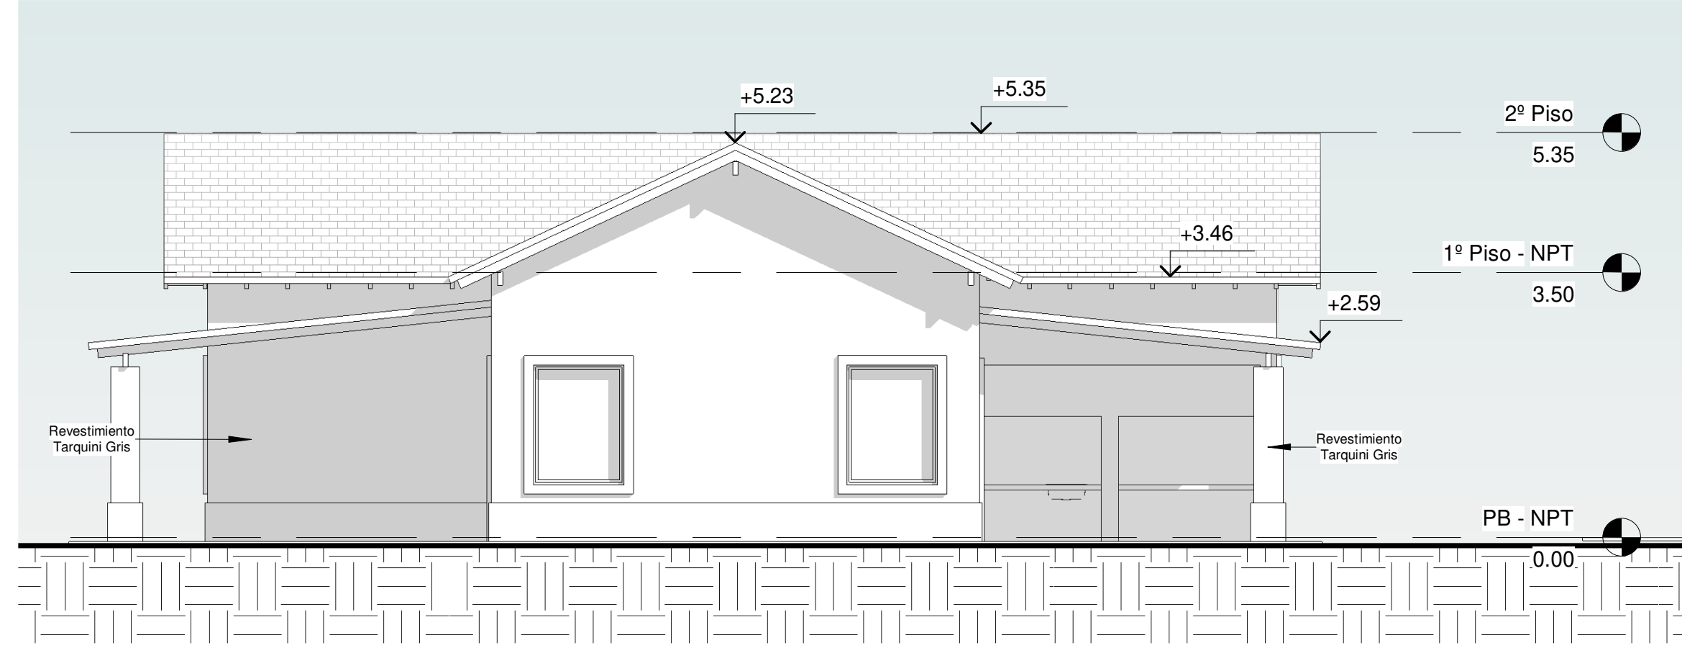

5 Vista Lateral Derecha

1 : 100

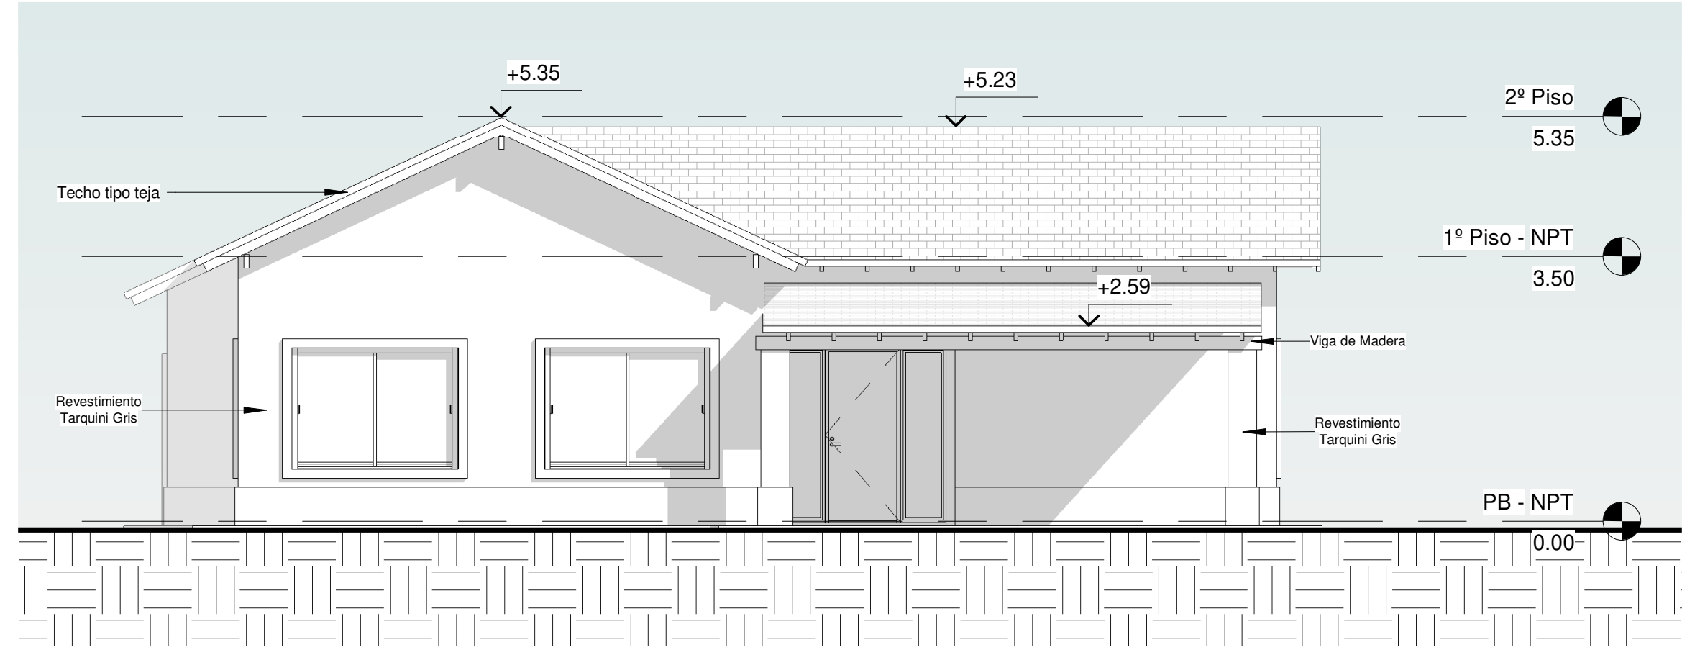

3 Vista Frente

1 : 100

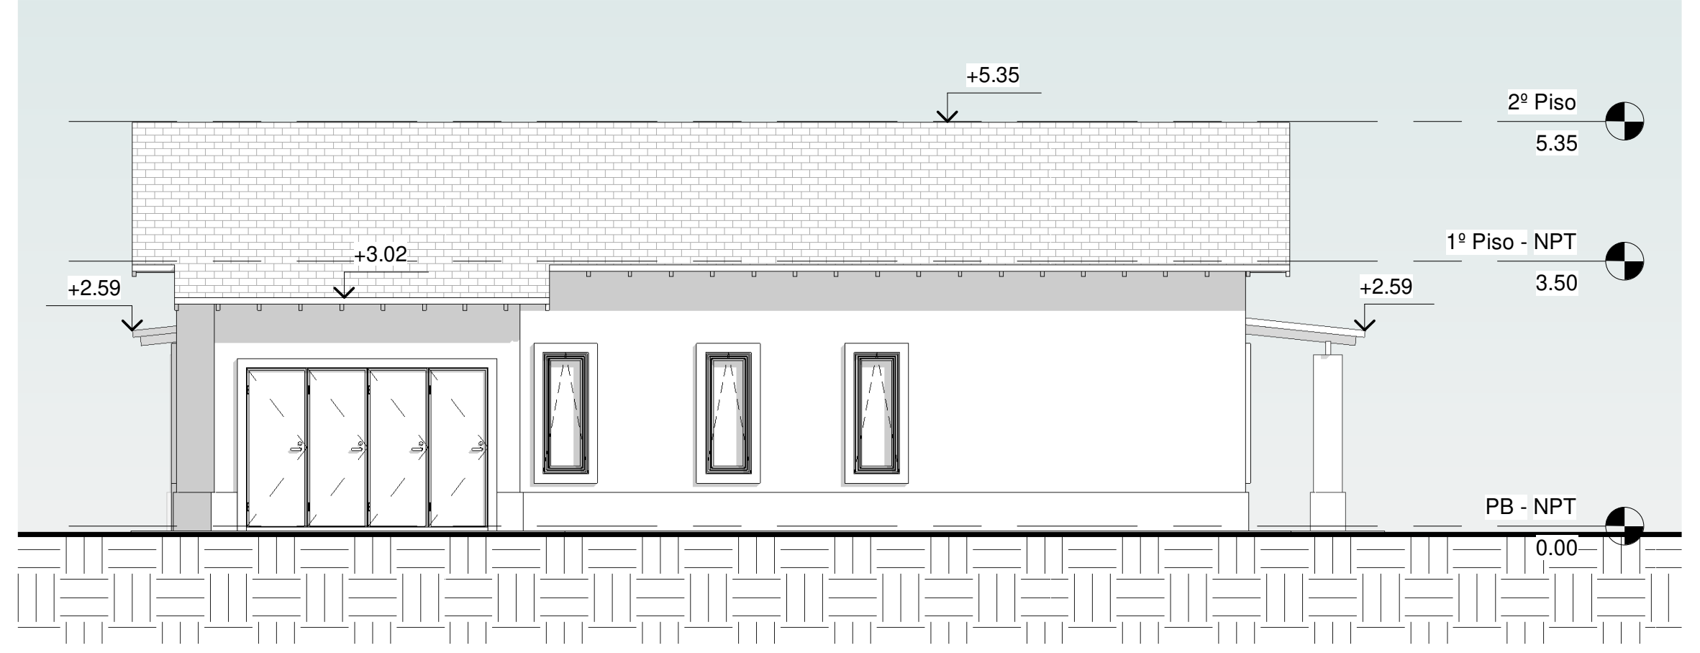

6 Vista Lateral Izquierda

1 : 100

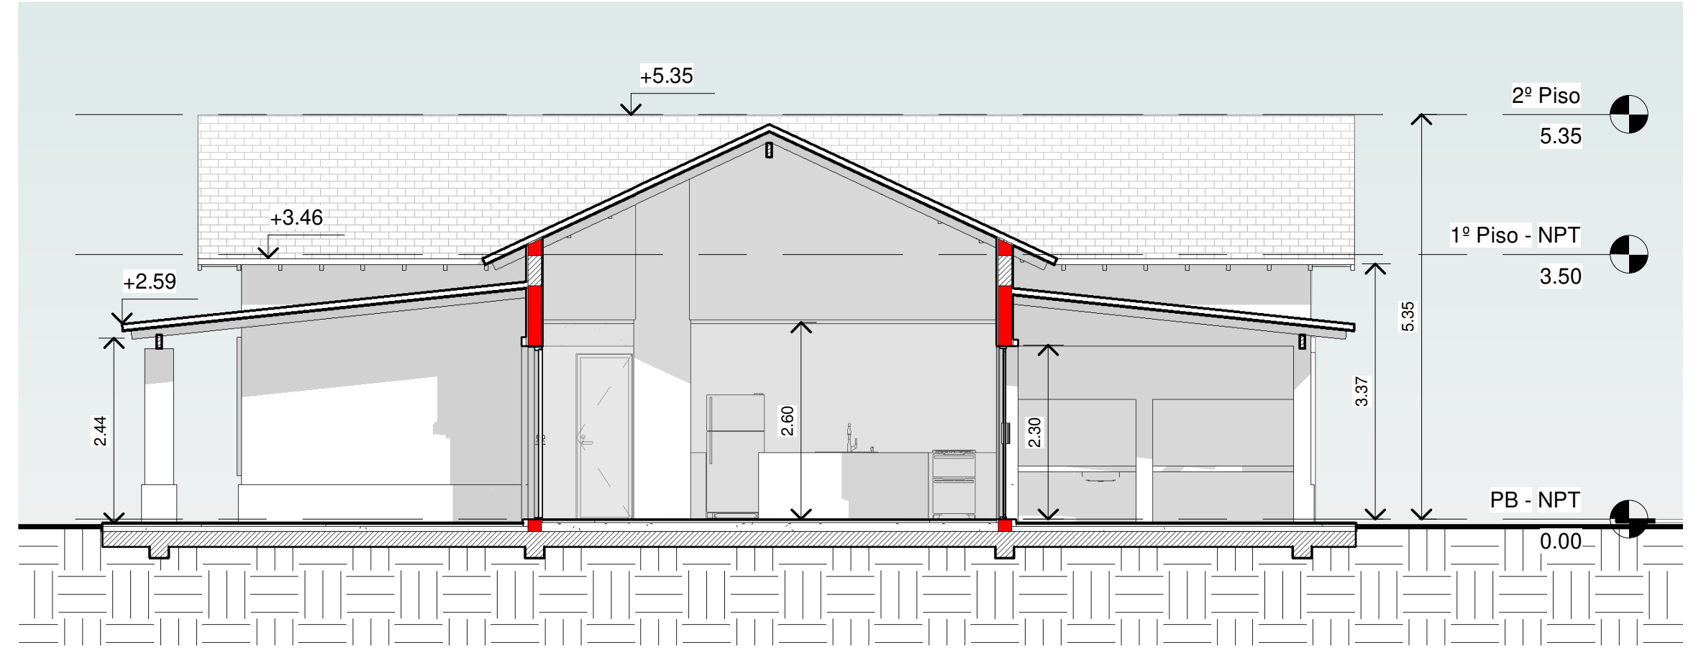

2 Corte A-A

1 : 100

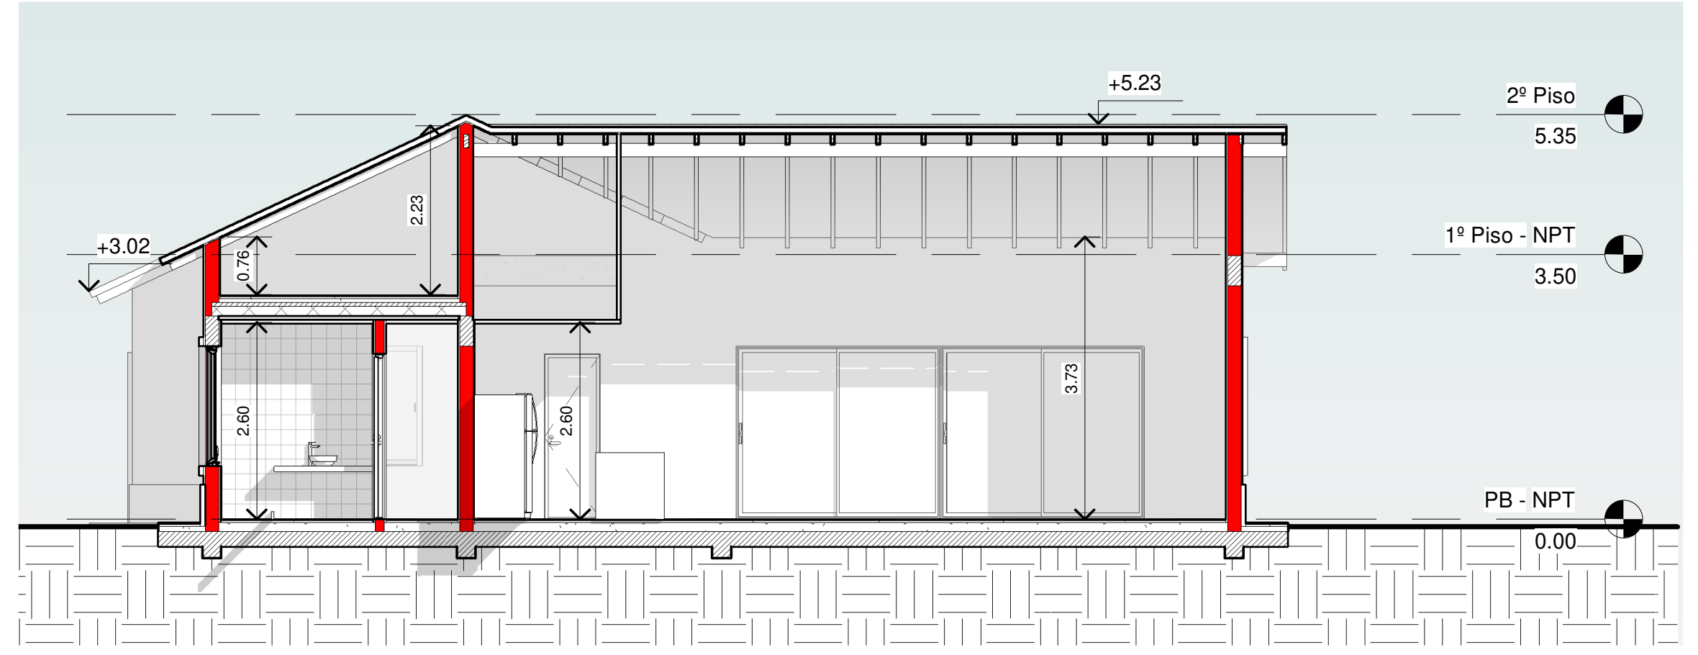

7 Corte B-B

1 : 100

CALCULO DE F.O.S. Y F.O.T.

$$F.O.S. = \frac{SUP.\ CUB.\ P.B. + SUP.\ SEMICUB.\ PB.}{SUP.\ TERRENO}$$

$$F.O.S. = \frac{209.42\ M2}{619.50\ M2}$$

F.O.S.= 0.338 CUMPLE C/REGLAMENTO DE EDIFICACION INTERNO

0.338 < 0.35 33.8% < 35%

$$F.O.T. = \frac{SUP.\ CUB. + SUP.\ SEMICUB.\ TOTAL}{SUP.\ TERRENO}$$

$$F.O.T. = \frac{209.42\ M2}{619.50\ M2}$$

F.O.T.= 0.338 CUMPLE C/REGLAMENTO DE EDIFICACION INTERNO

0.338 < 0.45 33.8% < 45%

BALANCE DE SUPERFICIES

POLIGONO	MEDIDAS LINEALES		CUBIERTA A CONSTRUIR PLANTA BAJA	SEMICUBIERTA A CONSTRUIR PLANTA BAJA	PILETA DE NATACION
	A	B			
01	4.05	0.94	3.80	0	0
02	14.14	6.96	98.41	0	0
03	4.32	6.58	0	28.42	0
04	6.44	6.78	43.66	0	0
05	5.34	6.58	0	35.13	0
06	3.50	8.00	0	0	28
	SUBTOTAL		145.87	63.55	28
	TOTALES				209.42

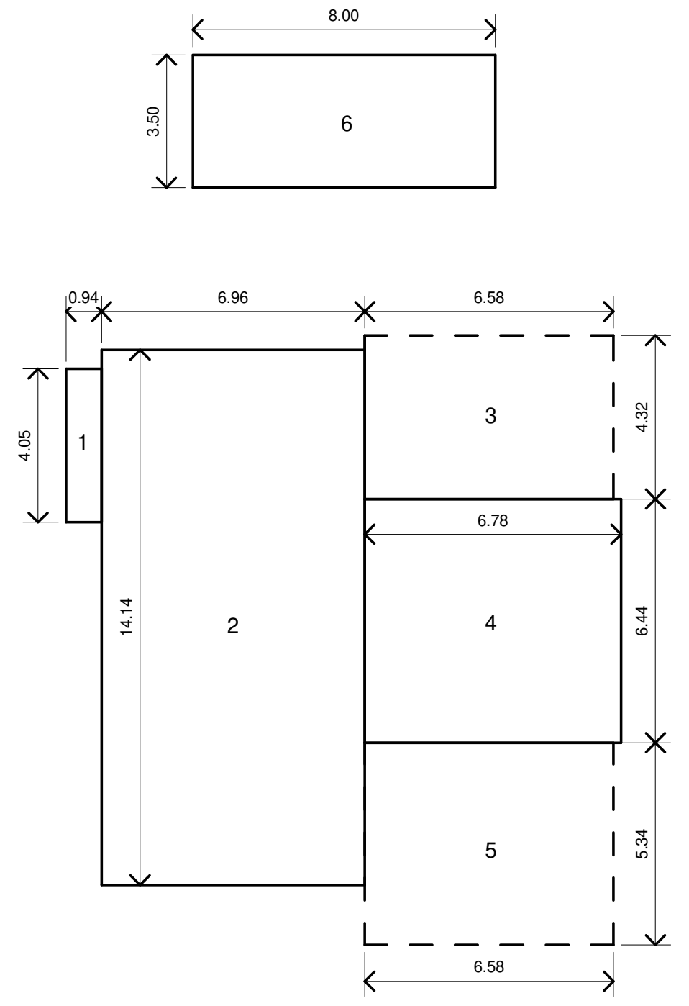

11 Poligonos PB

1 : 200

COLUMNAS Hº Aº

Pos. Nº	hp	Fb d1	Fb d2	Fb cm2	Fe cant	Fe ø	Fe cm2	Estribos ø	Estribos sep
C1	300	20	20	400	4	12	4.52	6	15

VIGAS DE ENCADENADO

Pos.	Forma	Q	L	Mto Tcm	Ra	Rb	bo	K2	M/bo	Raiz	h. calcul	H adop.	Fe adop	Fe cant	Fe Sec	Fe´ cant	Fe´ sec	1fe10	1fe12	1fe16	τ	Estribos 0	Estribos sep	Estribos 0	Estribos sep
VE	I	1	4	220	2.20	2.20	18	10.22	12	3.50	35.7	45.0	2.27	2	10	2	10	0.79	1.13	2.01	3.1	6	20	6	20

VIGAS DE ENCADENADO SUPERIOR

Pos.	Forma	Q	L	Mto Tcm	Ra	Rb	bo	K2	M/bo	Raiz	h. calculo	H adop.	Fe adop	Fe cant	Fe Sec	Fe´ cant	Fe´ sec	1fe10	1fe12	1f	τ	Estribos 0	Estribos sep
VES	I	1	3	124	1.65	1.65	18	10.22	7	2.62	26.8	45.0	1.28	2	10	2	10	0.79	1.13				

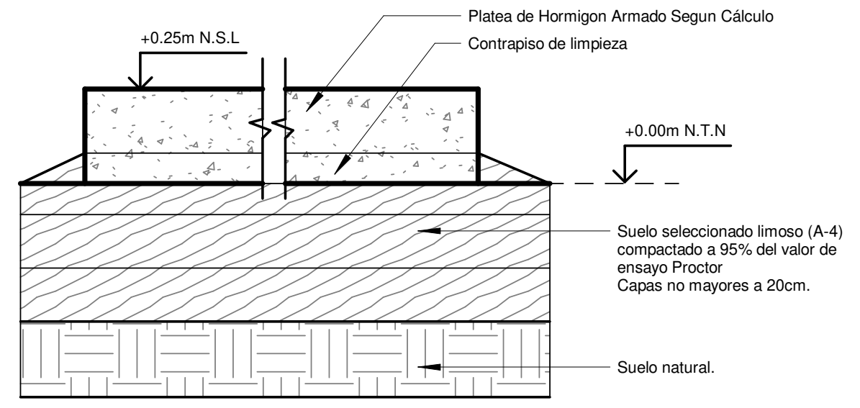
+0.25m N.S.L
Platea de Hormigon Armado Segun Cálculo
Contrapiso de limpieza
+0.00m N.T.N
Suelo seleccionado limoso (A-4) compactado a 95% del valor de ensayo Proctor Capas no mayores a 20cm.
Suelo natural.

DETALLE PLATEA

1 : 20

LOSAS CON LADRILLO CERAMICO

SE COLOCARA MALLA SOLDADA Q92 EN LA CAPA DE Ho.

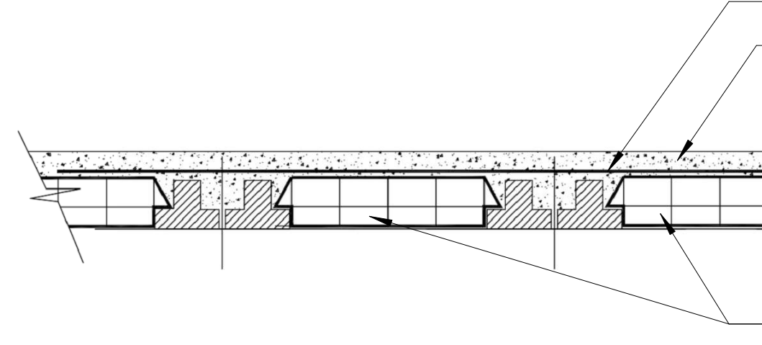

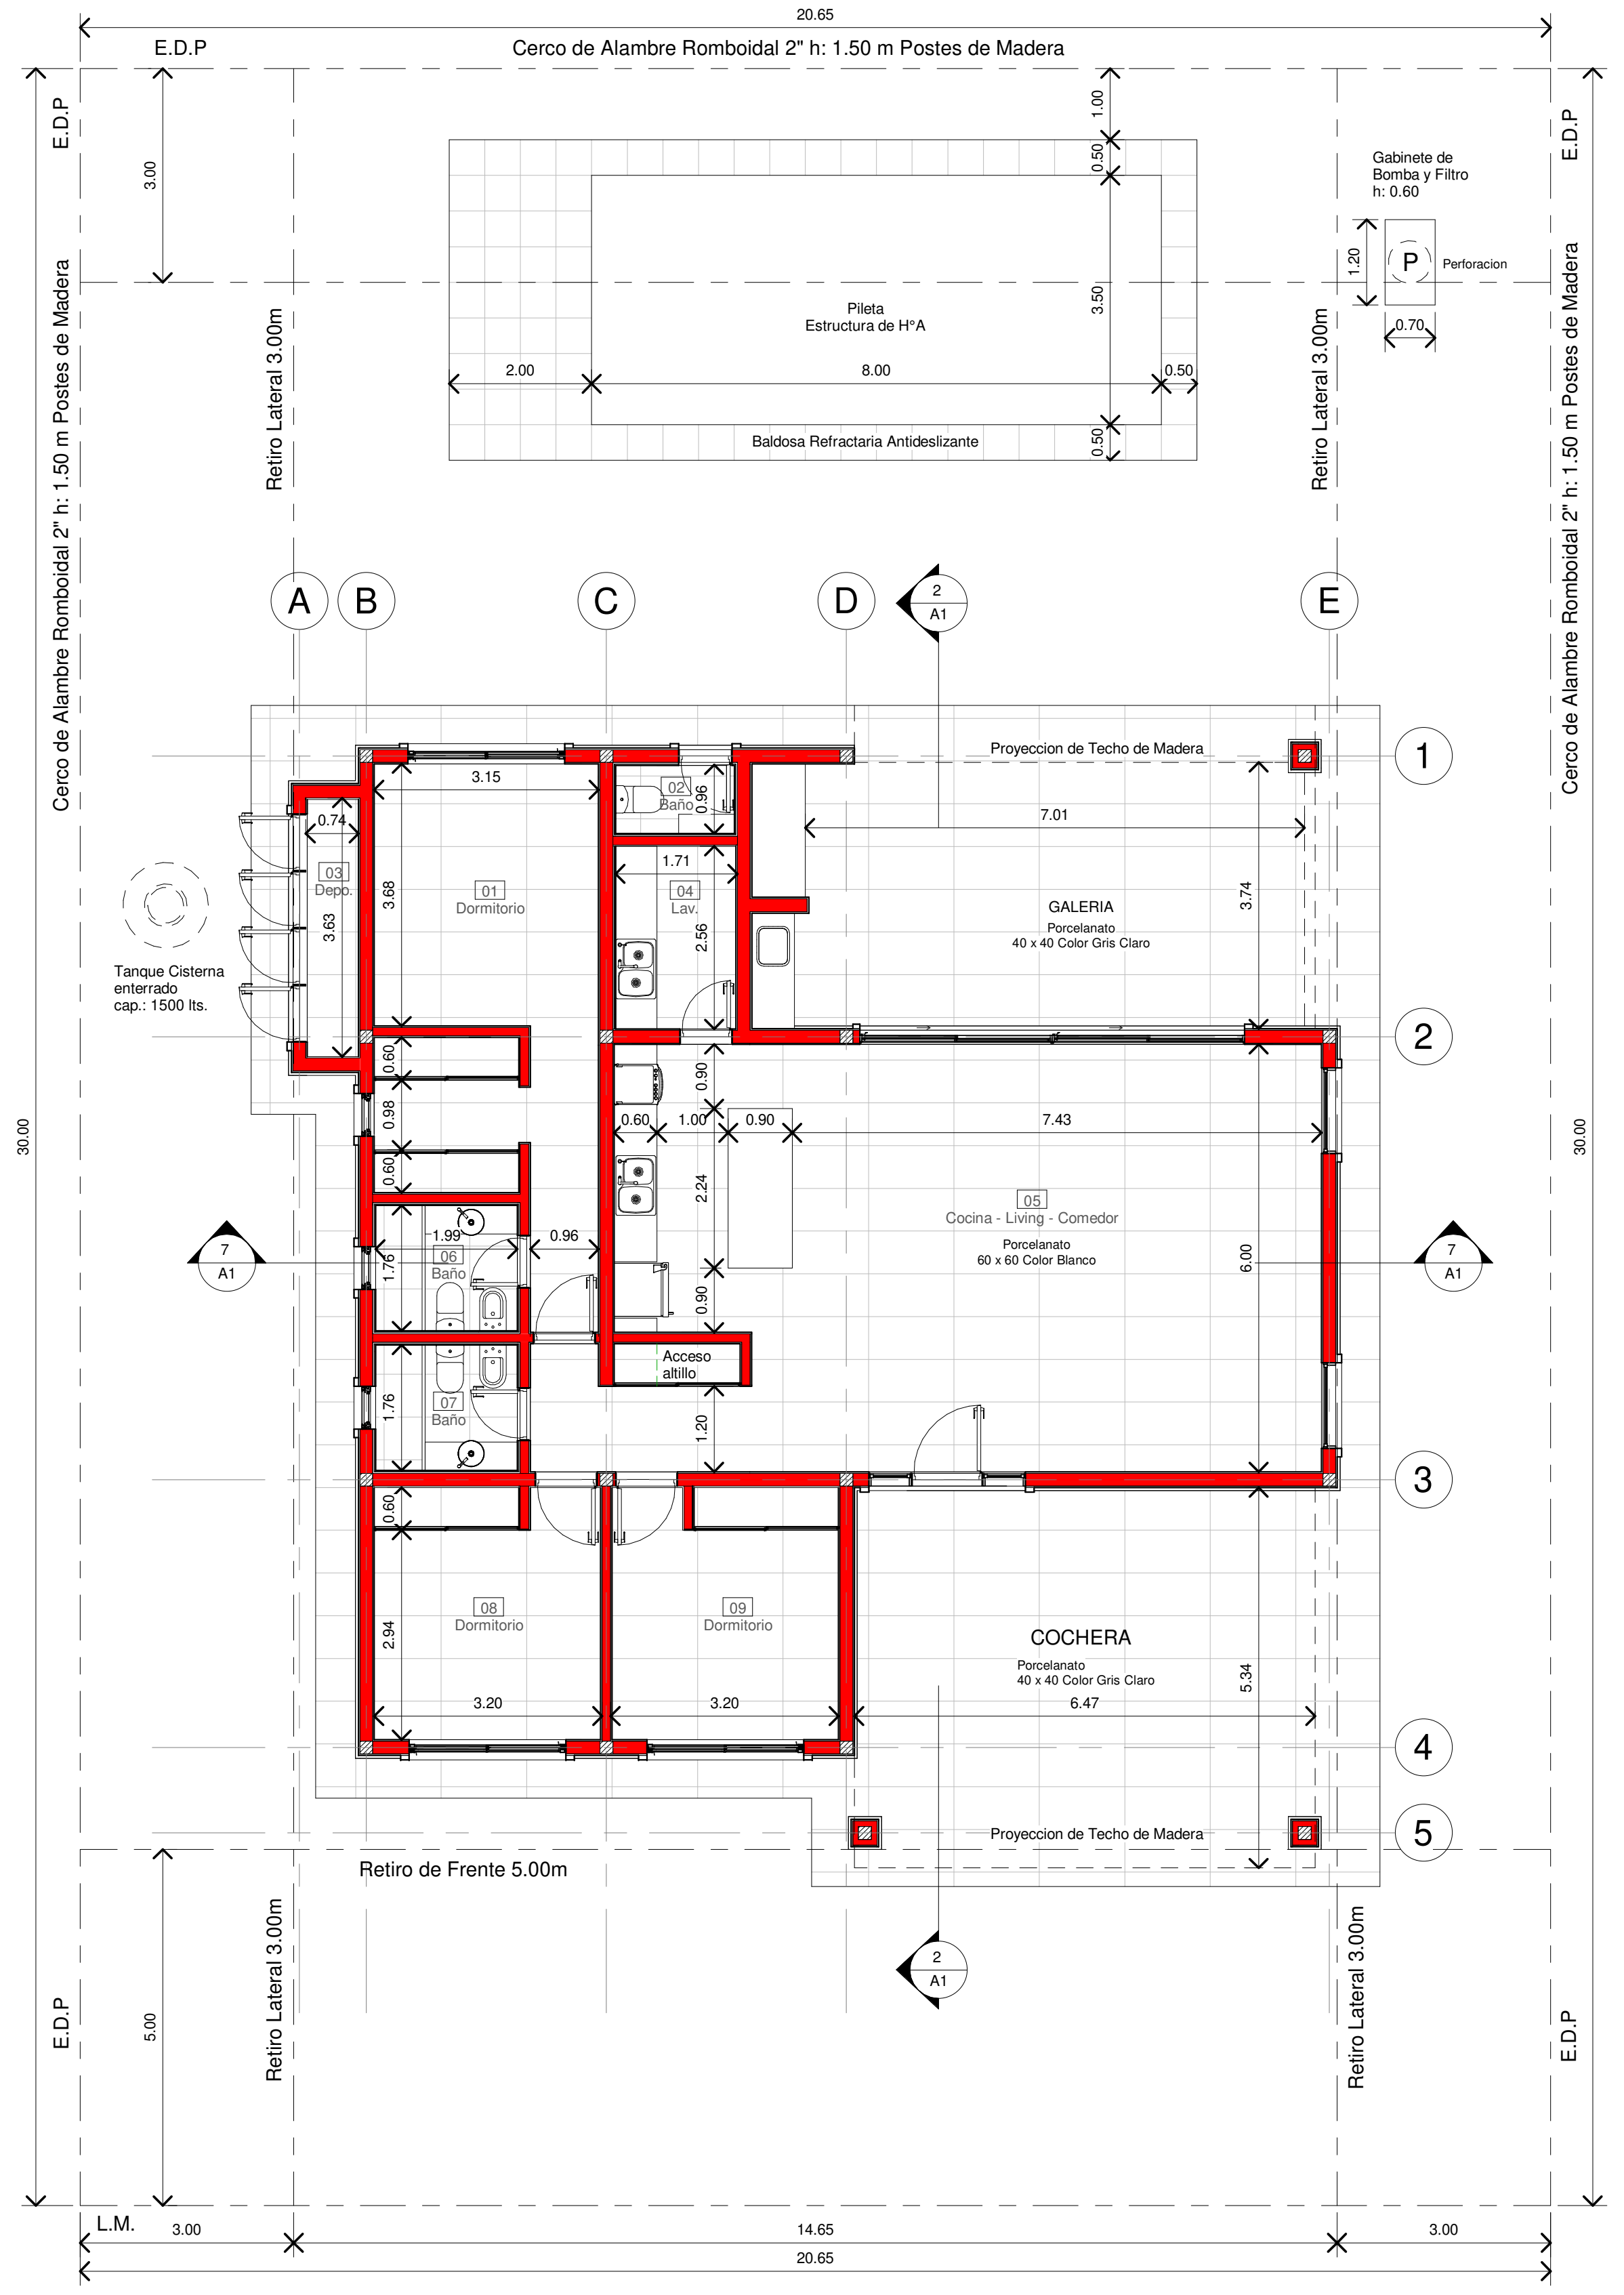
20.65
E.D.P
Cerco de Alambre Romboidal 2° h: 1.50 m Postes de Madera
Pileta Estructura de HºAº
Baldosa Refractaria Antideslizante
Gabinete de Bomba y Filtro
Retiro Lateral 3.00m
A
B
C
D
E
1
2
3
4
5
Proyeccion de Techo de Madera
GALERIA Porcelanato 60 x 40 Color Gris Claro
Dormitorio
Depo.
Lav.
Baño
Cocina - Living - Comedor Porcelanato 60 x 60 Color Blanco
Acceso
COCHERA Porcelanato 40 x 40 Color Gris Claro
Tanque Cisterna enterrado cap.: 1500 lts.
Retiro de Frente 5.00m
L.M.
3.00
14.65
3.00
30.00

1 PB - NPT

1 : 100

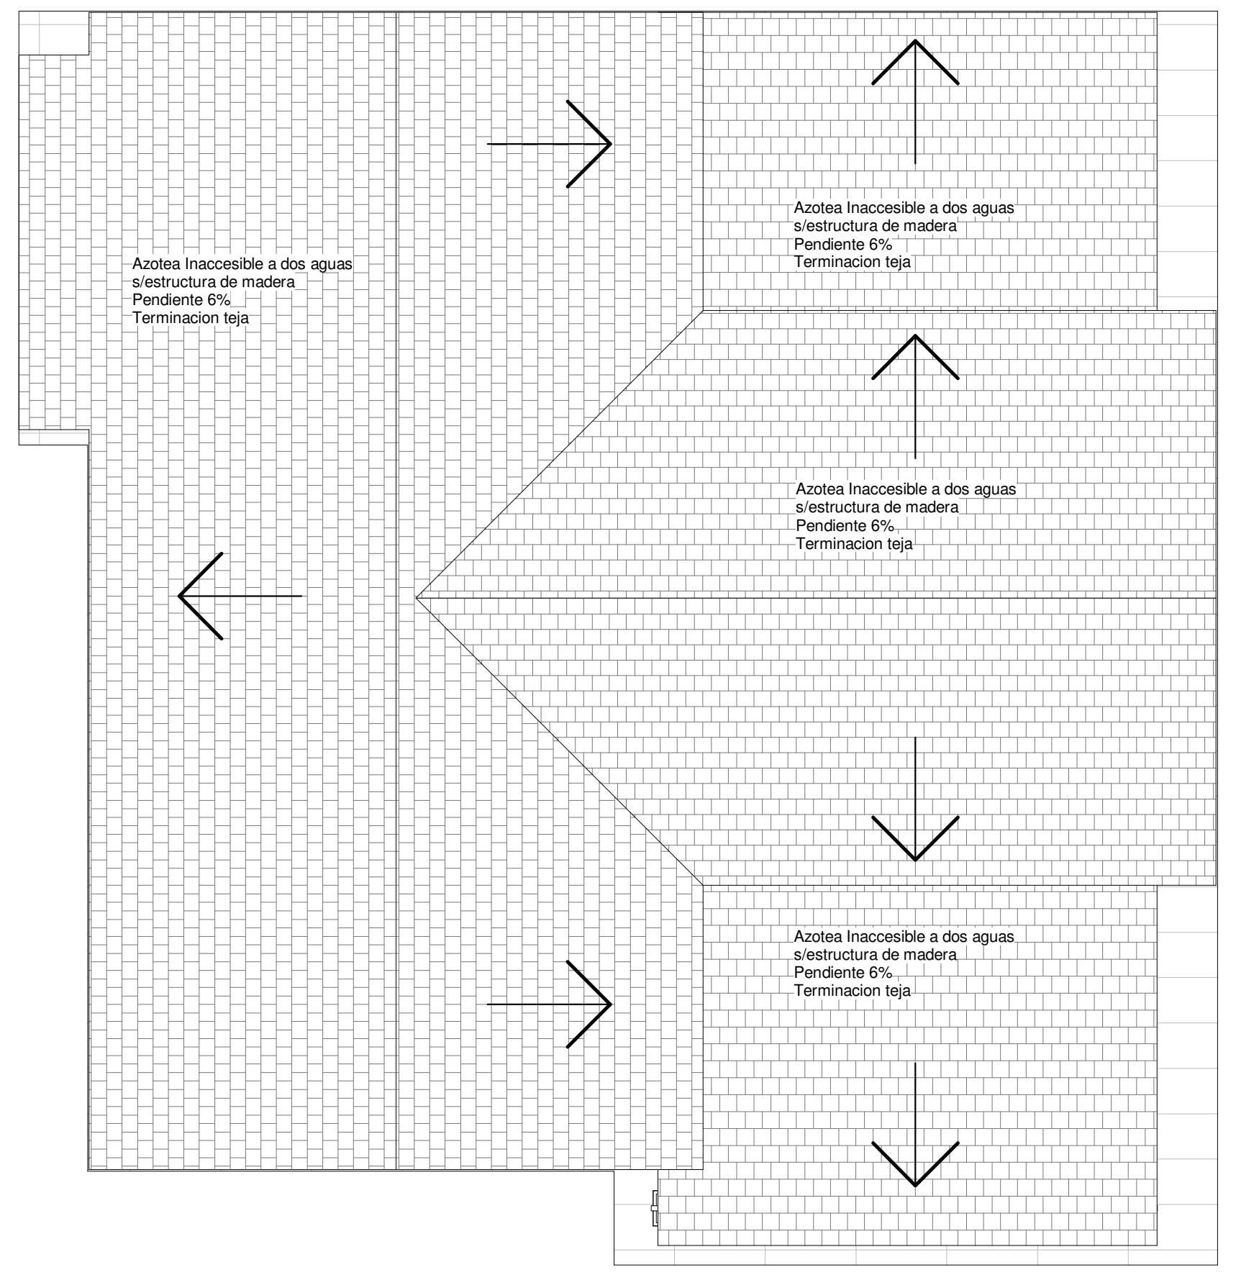
Azotea Inaccesible a dos aguas s/estructura de madera Pendiente 6% Terminacion teja

13 Planta de Techos

1 : 100

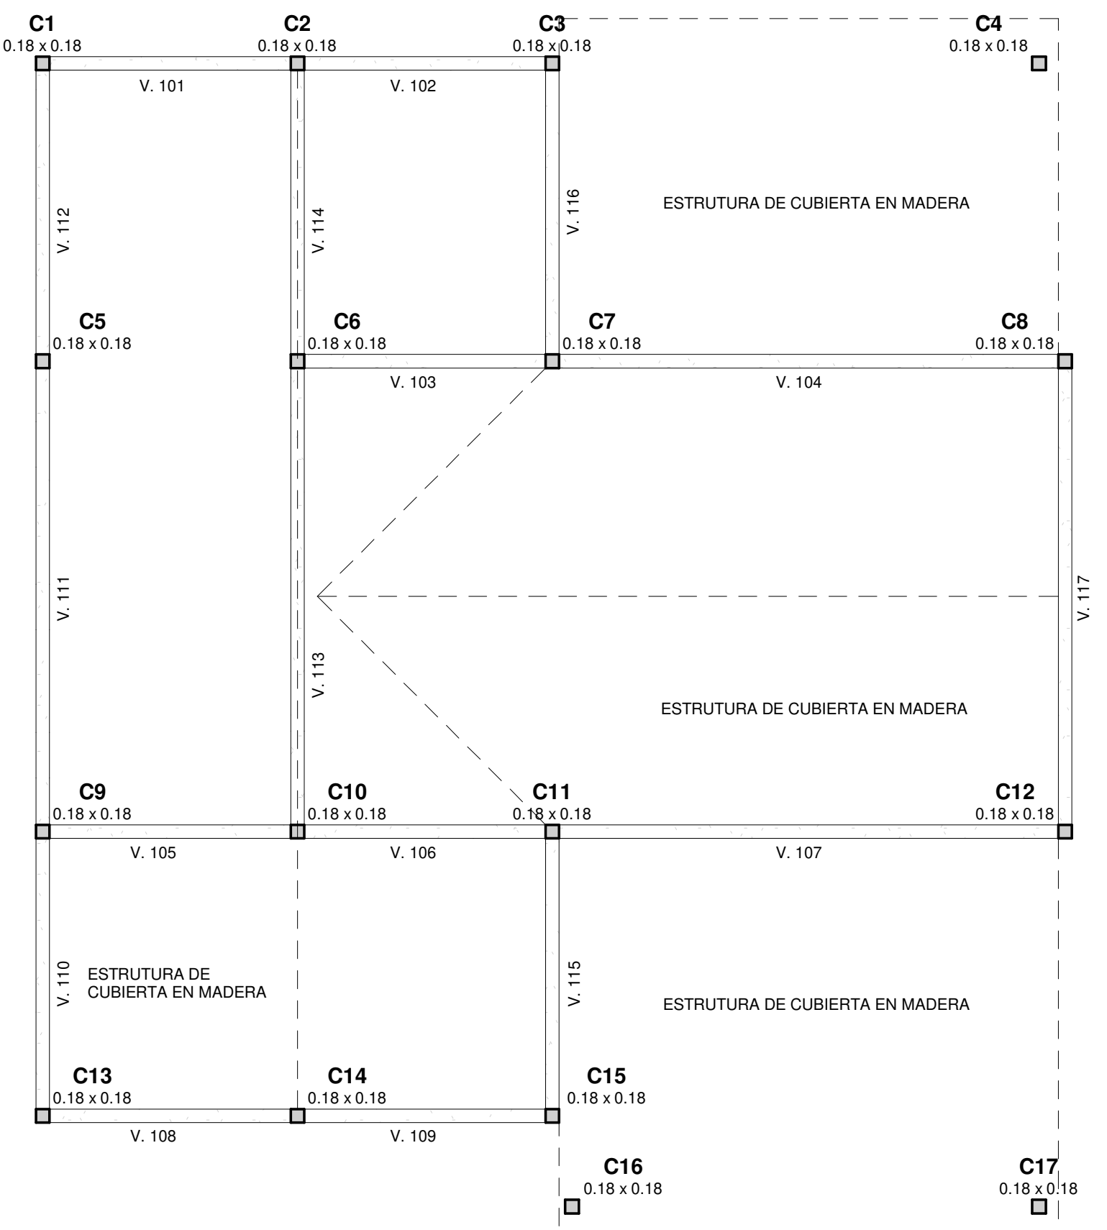

9 Estructura sobre PB

1 : 100

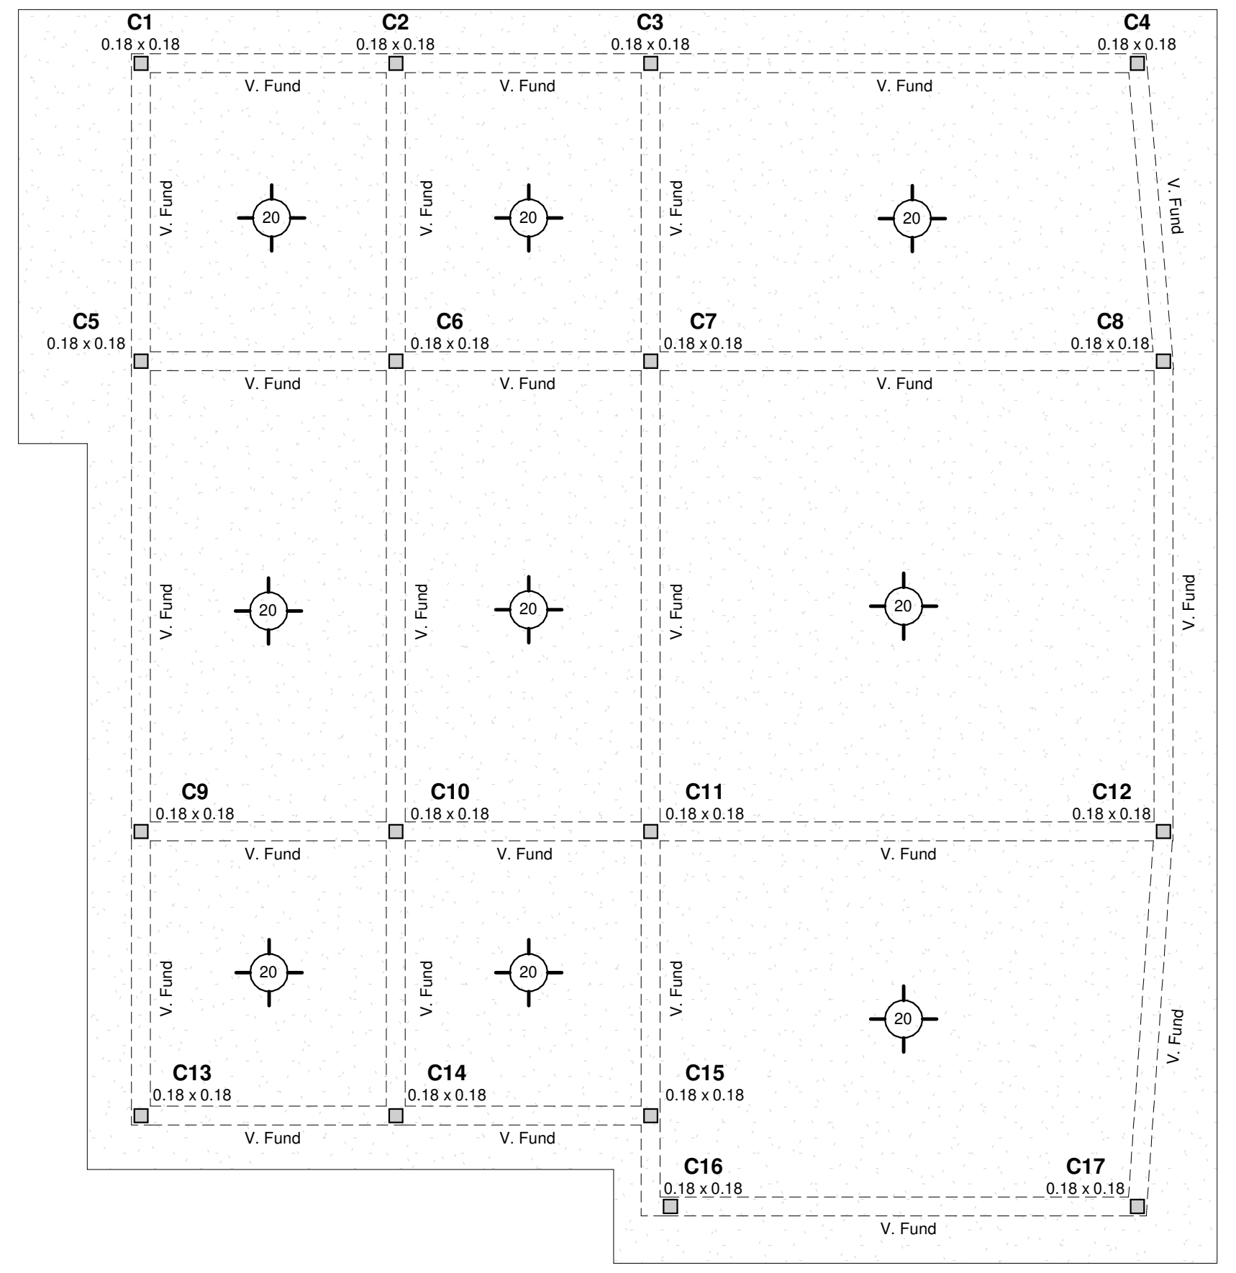

10 Estructura en Platea

1 : 100

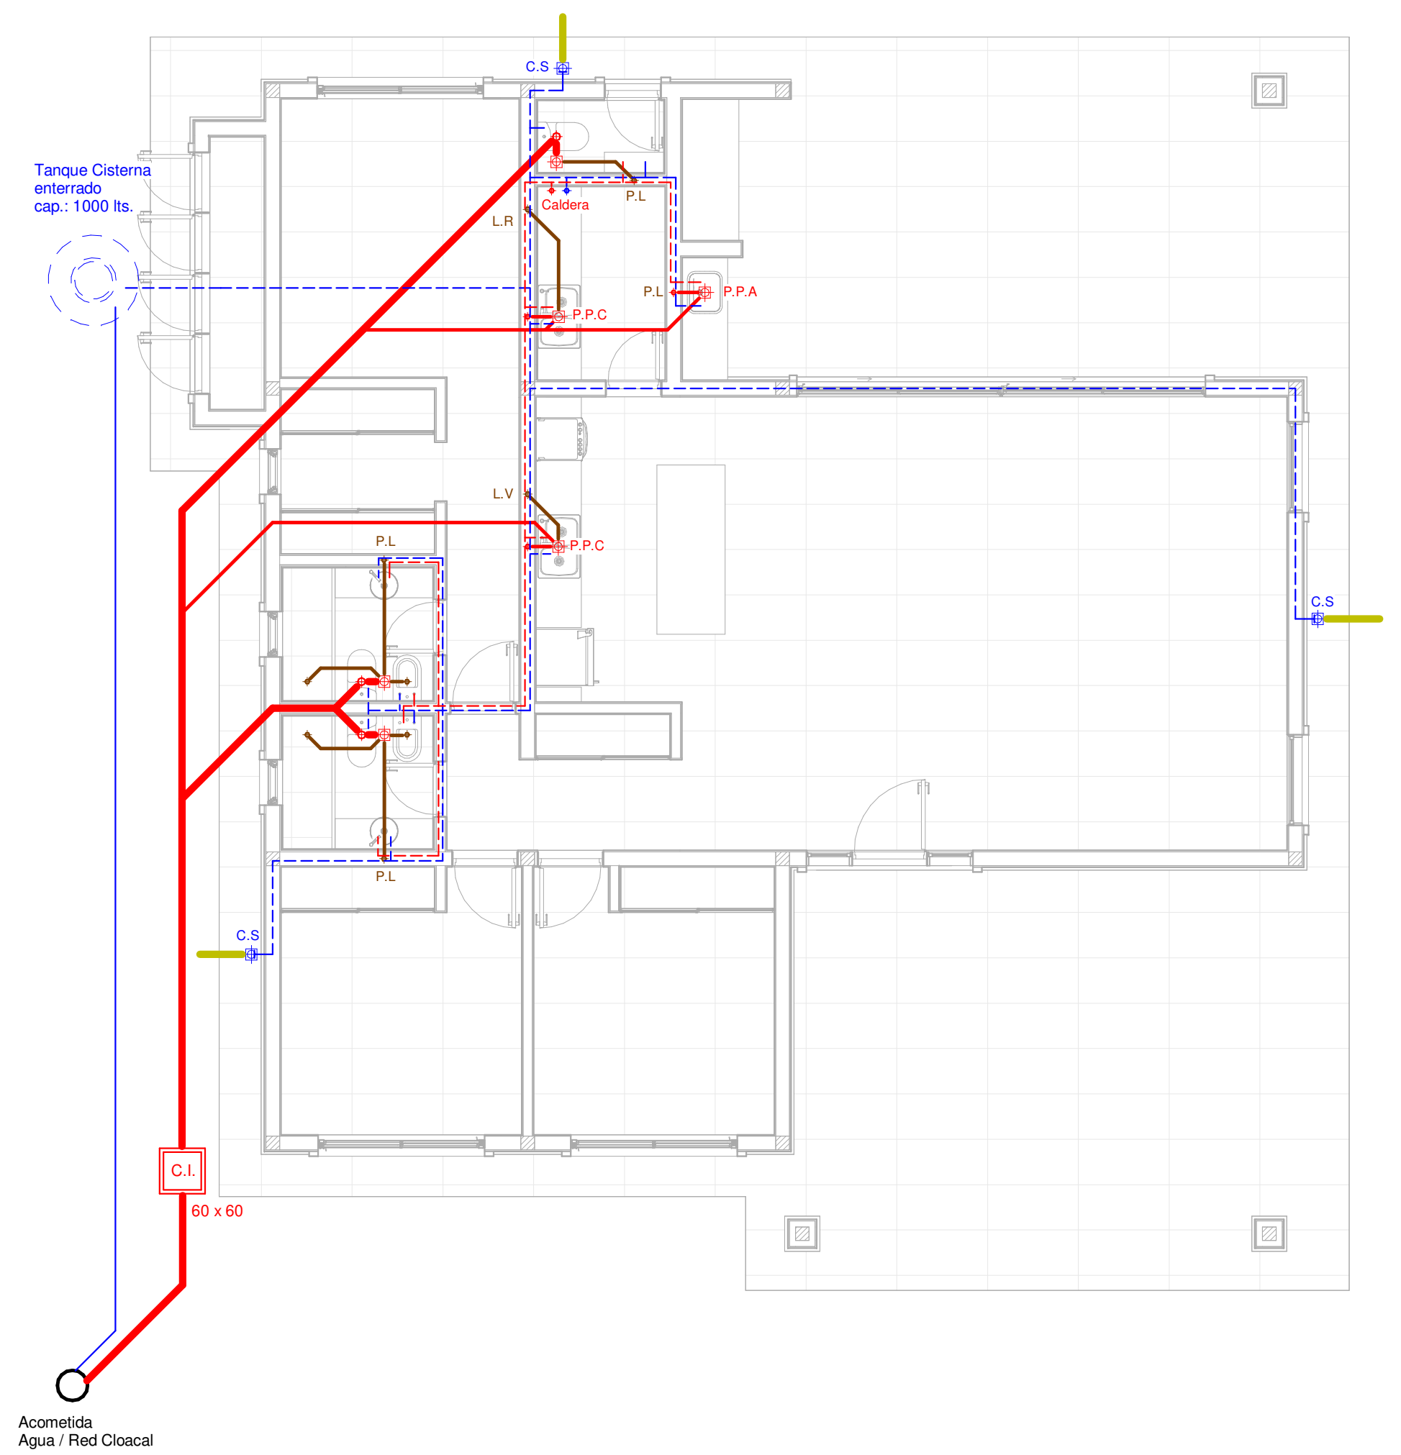
Tanque Cisterna enterrado cap.: 1000 lts
C.S
Acometida Agua / Red Cloacal

8 Instalacion Sanitaria PB

1 : 100

Expte.:	Letra:	Año: 2024	Pda.: 2504

Obra: A construir
Destino: Vivienda Unifamiliar
Propietario: Diego Alejandro Maldonado

Calle: ....
Localidad: Carlos Spegazzini
Partido: Ezeiza

Ubicación:

SEGUN CATASTRO		
CIRC.: III	SEC.: -	PARC.: 271d
Designacion Provisoria		UNID. PRIV.: 80
Zona Plan Regulador:		Según Título:
REX		

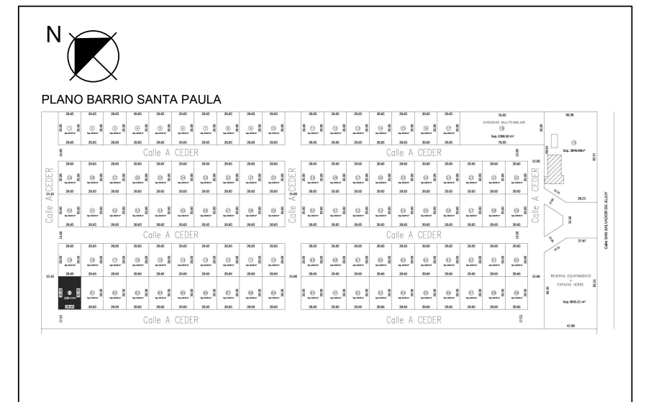

Superficies:

Sup. de la Sub Parcela	619.50 m2
Sup. Cubierta a Construir	145.87 m2
Sup. Semi Cubierta a Construir	63.55 m2
Sup. Total a Construir	209.42 m2
Sup. Libre	410.08 m2
Sup. de la Pileta	28.00 m2
F.O.S. Máximo: 0.35	F.O.S. Utilizado: 0.34
F.O.T. Máximo: 0.45	F.O.T. Utilizado: 0.34

Antecedentes:

Expte.: Letra: Año:

Propietario:
Diego Alejandro Maldonado
Dom.: Beron de Astrada 6633 - Villa Lugano - CABA

Firma:

Proyecto:
Oscar Humberto Tevez
Mat. Nac. T-49877 MAT.MUN.: 2763 CUIT:
Domicilio: 14 E/31 y 32 #350 - Pte Peron
Firma:

Dirección:
Oscar Humberto Tevez
Mat. Nac. T-49877 MAT.MUN.: 2763 CUIT:
Domicilio: 14 E/31 y 32 #350 - Pte Peron
Firma:

Construcción:
Oscar Humberto Tevez
Mat. Nac. T-49877 MAT.MUN.: 2763 CUIT:
Domicilio: 14 E/31 y 32 #350 - Pte Peron
Firma:

LOS CALCULOS DE ESTRUCTURA SON DE EXCLUSIVA RESPONSABILIDAD DE LOS PROFESIONALES ACTUANTES.
LA APROBACION DE LOS PLANOS NO IMPLICA LA HABILITACION DE LA FINCA O LOCAL.

NOTA BOMBEROS
Cumplira Art. 4.12 (prevencion contra incendios segun CE.)
Contara con salida de emergencia claramente señalizada con herraje antipanico
Y luces de emergencia indicando el recorrido hacia la misma.
Contara con luces de emergencia en circulaciones comunes y zona de estacionamiento.